


FINISH SCHEDULE					
PAINT					
KEY	FINISH / MATERIAL	COLOR / STYLE	FINISH	MANUFACTURER	LOCATION / REMARKS
P 1	2 COATS PAINT - OVER 1 COAT SW ALL PURPOSE LATEX PRIMER	SW SNOWBOUND 7004	WALL/TRIM - EGGSHELL CEILING - FLAT	SHERWIN WILLIAMS	INTERIOR WALLS AS NOTED, CEILING AS NOTED, INTERIOR TRIM ELEMENTS
P 2	2 COATS PAINT - OVER 1 COAT SW ALL PURPOSE LATEX PRIMER	SW PEPPERCORN 7674	WALL/TRIM - EGGSHELL CEILING - FLAT	SHERWIN WILLIAMS	CEILING TROUGH AS NOTED, BOH DOOR/BACK VEST. WALL, SALES FLOOR WALLS AND ELEMENTS ABOVE 12'-0" A.F.F.
P 3	2 COATS PAINT - OVER 1 COAT SW ALL PURPOSE LATEX PRIMER	SW SPLASHY 6942	WALL/TRIM - EGGSHELL CEILING - FLAT	SHERWIN WILLIAMS	SALES DIGITAL SCREEN RECESS AT WALLPAPER WALL, TOILET ROOM DOOR, STOREFRONT AS NOTED
P 4	2 COATS PAINT - OVER 1 COAT SW ALL PURPOSE LATEX PRIMER	SW ACCESSIBLE BEIGE 7036	WALL/TRIM - EGGSHELL CEILING - FLAT	SHERWIN WILLIAMS	NOT USED
P 5	2 COATS PAINT - OVER 1 COAT SW ALL PURPOSE LATEX PRIMER	SW TRICORN BLACK 6258	WALL/TRIM - EGGSHELL CEILING - FLAT	SHERWIN WILLIAMS	STOREFRONT DIGITAL SCREEN RECESS
P 6	2 COATS PAINT - OVER 1 COAT SW ALL PURPOSE LATEX PRIMER	SW STURDY BROWN 6097	WALL/TRIM - EGGSHELL CEILING - FLAT	SHERWIN WILLIAMS	NOT USED
METAL					
KEY	FINISH / MATERIAL	COLOR / STYLE	FINISH	MANUFACTURER	LOCATION / REMARKS
M 1	16 GAUGE OR RIGID BACKED BRUSHED STAINLESS STEEL	CLEARCOAT	BRUSHED	---	NOT USED
M 2	ANODIZED ALUMINUM STOREFRONT	DARK BRONZE	ANODIZED	---	EXTERIOR STOREFRONT SYSTEM
M 3	POWDERCOATED METAL	SW SPLASHY 6942	POWDERCOATED	---	EDGE TRIM AT STAGE AS NOTED, WALLPAPER SCREEN RECESS TRIM, EDGE TRIM AT PLANK AS NOTED
M 4	POWDERCOATED METAL	BLACK	POWDERCOATED	---	STOREFRONT SCREEN RECESS TRIM, EDGE TRIM AT PLANK AS NOTED
WOOD					
KEY	FINISH / MATERIAL	COLOR / STYLE	FINISH	MANUFACTURER	LOCATION / REMARKS
W 1	6 1/2" WIDE X 3/8" THICK LIGHT COLOR ENGINEERED HARDWOOD PLANK	LOVESAC OAK 1089 HARBOR	PREFINISHED (REPEL WATER RESIST)	SHAW	USE STAGGERED END JOINTS; STAGE (FIXTURE FF/1A AND FF/1B)
W 2	6 1/2" WIDE X 3/8" THICK DARK COLOR ENGINEERED HARDWOOD PLANK	LOVESAC HICKORY 7097 TRANQUILITY	PREFINISHED (REPEL WATER RESIST)	SHAW	INTERIOR DISPLAY/ENTRY WALLS AND SOFFIT
VINYL					
KEY	FINISH / MATERIAL	COLOR / STYLE	FINISH	MANUFACTURER	LOCATION / REMARKS
V 1	12" X 12" X 1/8" VINYL COMPOSITION TILE FLOORING	STANDARD EXCELON IMPERIAL TEXTURE DESERT BEIGE 51809	---	ARMSTRONG	BOH FLOORING, TOILET ROOM FLOORING
V 2	7" X 48" X 3/8" RESILIENT LUXURY VINYL FLR PLANK WITH CORK UNDERLAY	ADESA 1424V CABIN-V2 00100	PREFINISHED (EXO GUARD)	PATCRAFT	NOT USED
TILE					
KEY	FINISH / MATERIAL	COLOR / STYLE	GROUT	MANUFACTURER	LOCATION / REMARKS
T 1	8" X 48" X 3/8" LIGHT COLOR WOOD GRAIN PLANK PORCELAIN TILE	CS50H WHITE OAK 00100	LATICRETE #90 (LIGHT PEWTER)	PATCRAFT	USE STAGGERED END JOINTS, 1/8" MAX. GROUT LINE BTWN JOINTS; SALES FLOORING
T 2	12" X 12" CERAMIC FLOOR TILE	BRIXTON BONE BX01	LATICRETE #23 (ANT. WHITE)	DALTILE	NOT USED
T 3	6" X 36" X 3/8" DARK COLOR WOOD GRAIN PLANK PORCELAIN TILE	CREEKWOOD LOVT3 WALNUT 0700	LATICRETE SPECTRALOCK PRO PREMIUM #60 (DUSTY GREY)	PATCRAFT	NOT USED
SPECIAL WALL FINISH					
KEY	FINISH / MATERIAL	COLOR / STYLE	FINISH	MANUFACTURER	LOCATION / REMARKS
SP 1	3/8" THICK WHITE THIN BRICK	ANTIQUE BRICK 2920, PAINTED TO MATCH P/1	---	BRICK MY WALLS	3/8" MIN. GROUT JOINT BTWN BRICKS, USE CORNER BRICK AT OUTSIDE CORNERS; SALES WALLS AS NOTED
SP 2	CUSTOM GRAPHIC WALLPAPER	CUSTOM	VELVET	---	GW6 BENEATH WALLCOVERING TO HAVE LEVEL 5 FINISH; SALES WALL WITH SCREEN RECESS AS NOTED
SP 3	3/8" THICK FRP WALL PANELING	SEQUENTIA EMBOSSED WHITE 1130	---	CRANE COMPOSITES	SEQUENTIA EMBOSSED WHITE FRP OR SIM; DRINKING FOUNTAINS, MOP SINKS, AND RESTROOMS AS NOTED
NOTE - FINISH SCHEDULE DOES NOT INCLUDE COMPLETE LIST OF FINISHES ON ITEMS FURNISHED WHOLE FROM INDEPENDENT FABRICATORS SUCH AS SIGNAGE AND FIXTURES. SEE FIXTURE SHOP DRAWINGS FOR FINISH DESCRIPTIONS AND ADDITIONAL INFORMATION.					

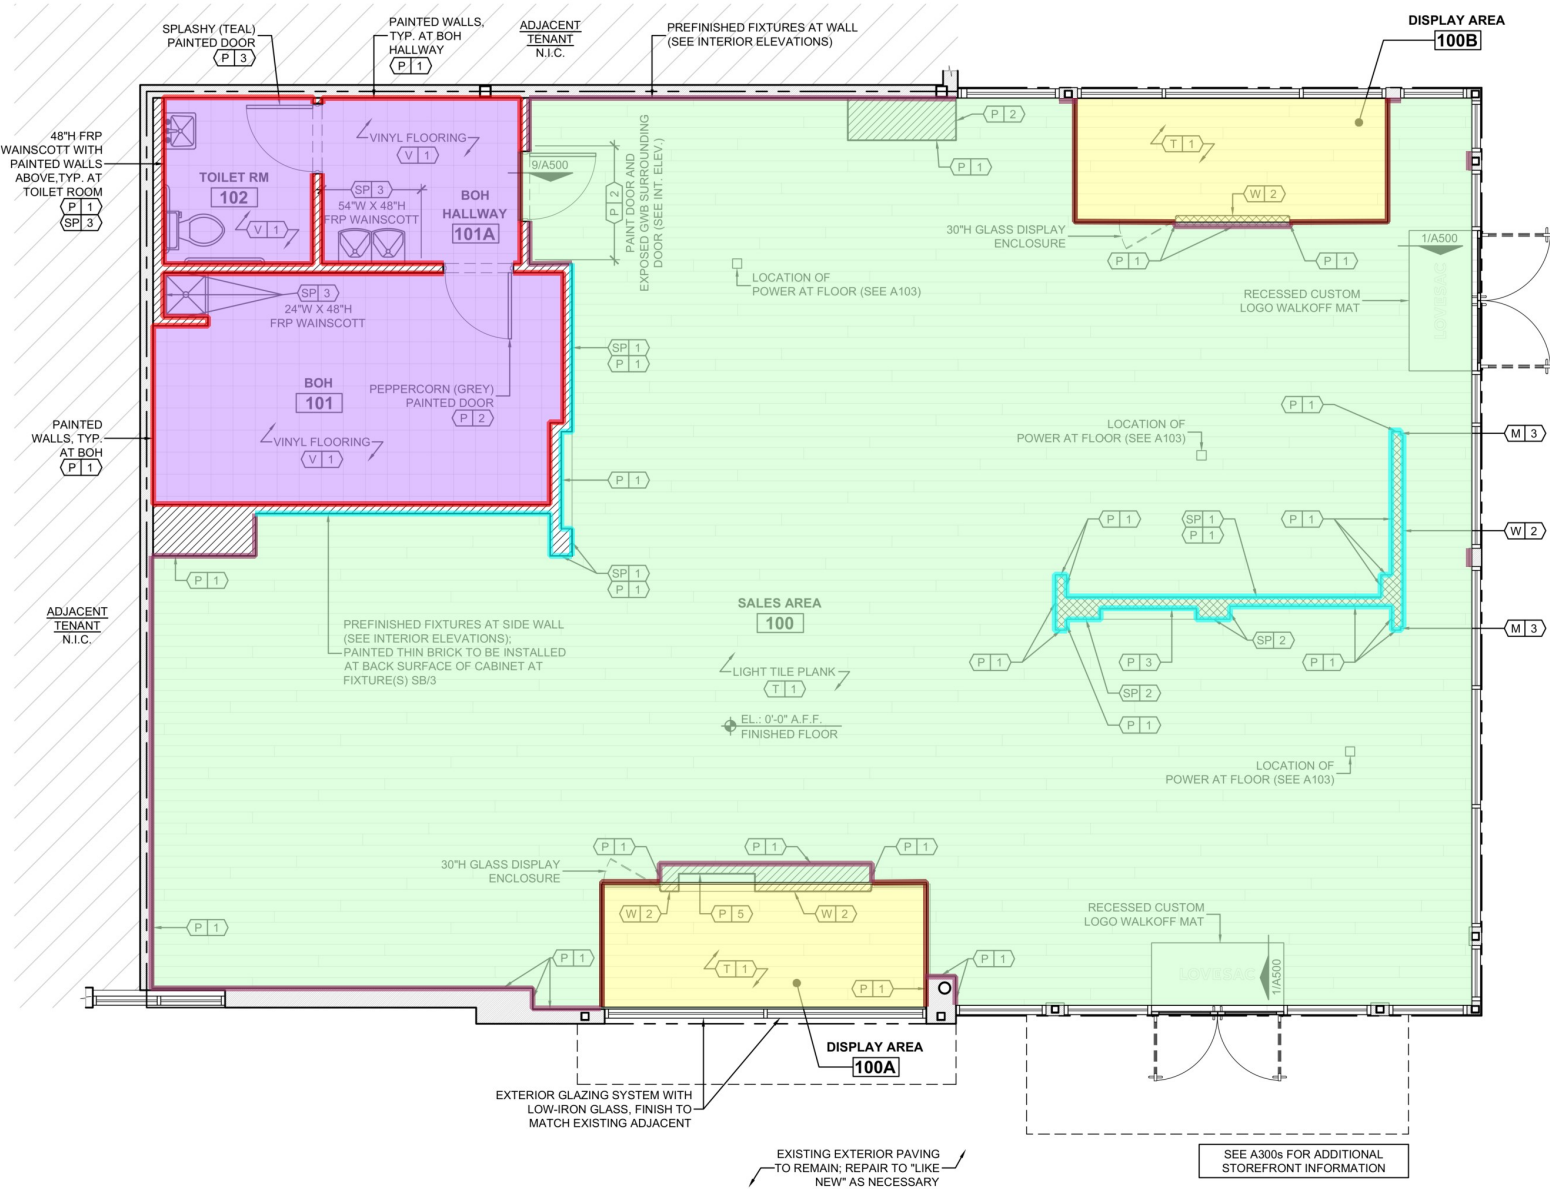

1 FINISH PLAN

A101 SCALE: 1/4"=1'-0"

NOTES

- REFER TO CONSTRUCTION PLAN (SEE A100) FOR CONSTRUCTION SCOPE OF WORK.
- REFER TO STOREFRONT DRAWINGS (SEE A300s) FOR STOREFRONT FINISHES.
- REFER TO INTERIOR ELEVATIONS (SEE A400s) FOR WALL AND MILLWORK FINISHES.
- REFER TO RCP (SEE A200) FOR CEILING FINISHES.